


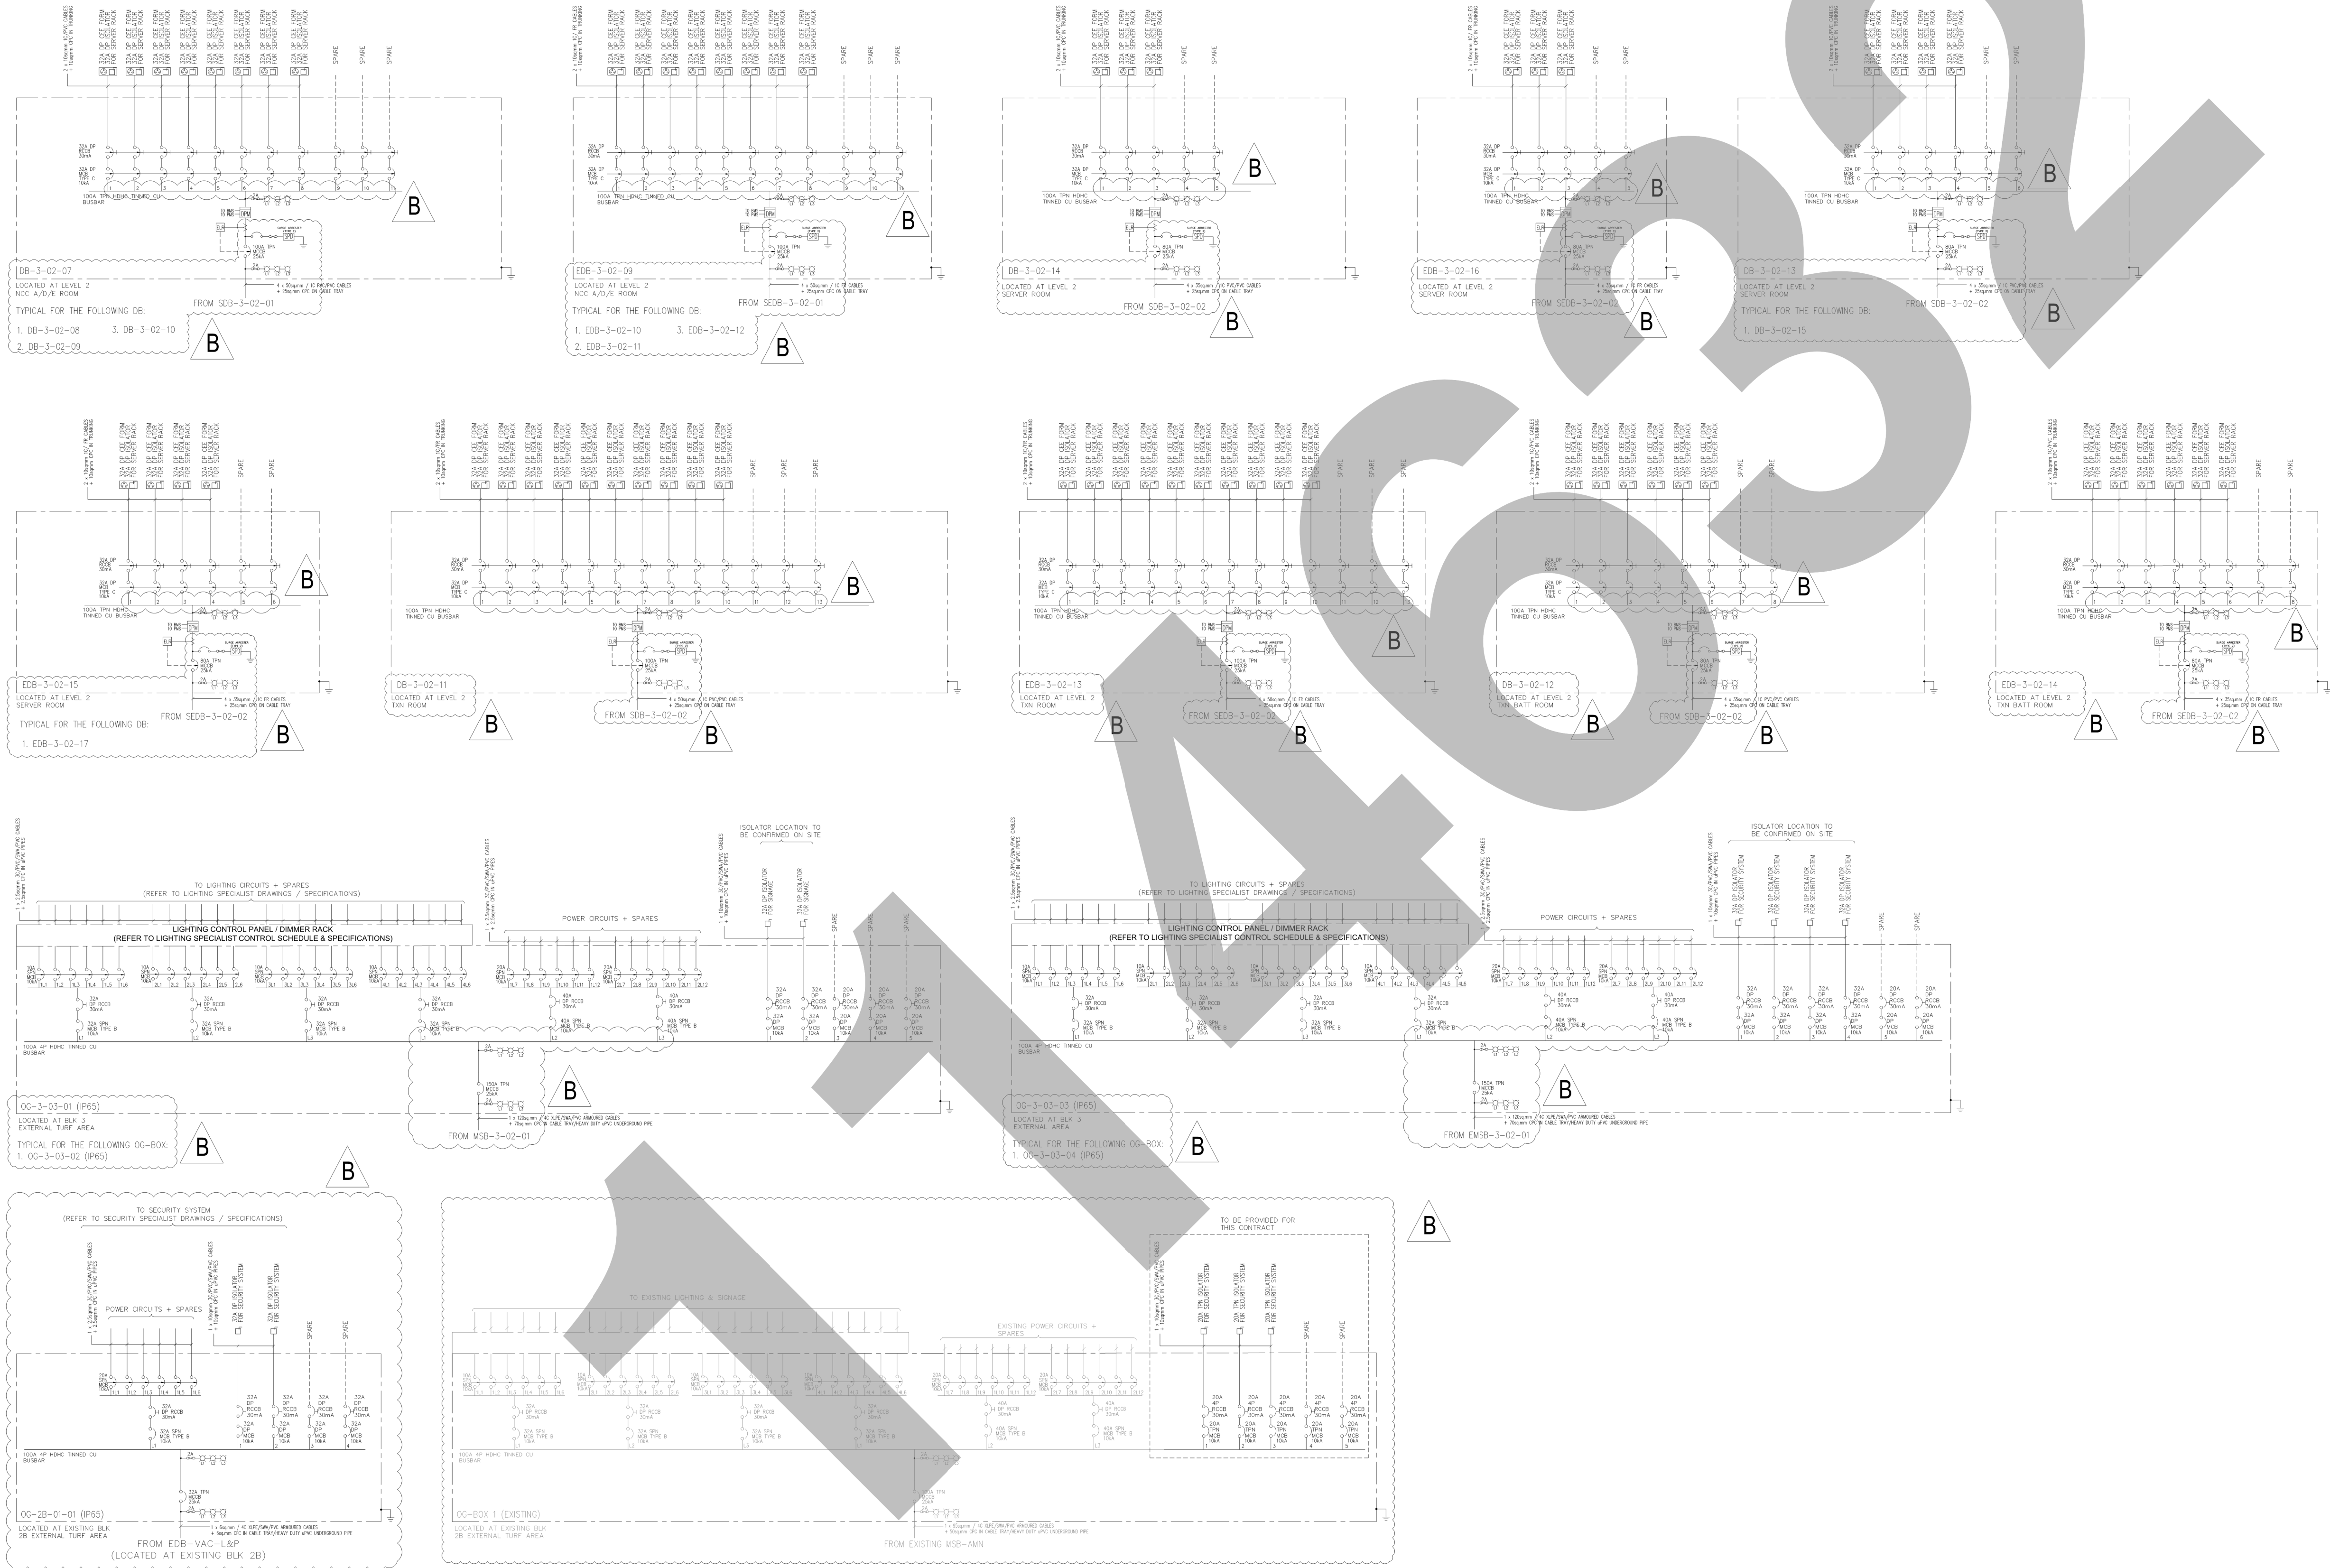

SINGLE LINE DIAGRAM (2 OF 28)

SCALE N.T.S

NOTE:
ALL WORKS AND SCOPE MENTIONED AND INDICATED ON THE DRAWINGS, SCHEDULE, CUTSHEET AND SPECIFICATIONS SHALL BE BY CONTRACTOR UNLESS OTHERWISE STATED

FOR TENDER ONLY		
DATE	REV	DESCRIPTION
15.09.2025	A	ISSUED FOR CORRIGENDUM 2
17.10.2025	B	ISSUED FOR CORRIGENDUM 4

ACOUSTICS CONSULTANT
ALPHA ACOUSTICS ENGINEERING PTE LTD
300 BEACH ROAD
#03-00 THE CONCOURSE
SINGAPORE 199555
TEL: +65 62992466 FAX: +65 62990297

LIGHTING CONSULTANT
DP LIGHTING PTE LTD
6 RAFFLES BOULEVARD
#02-249 MARINA SQUARE
SINGAPORE 039594
TEL: +65 6338 3988 FAX: +65 6337 9989

FACADE ENGINEERING CONSULTANT
DP FACADE PTE LTD
6 RAFFLES BOULEVARD
#02-249 MARINA SQUARE
SINGAPORE 039594
TEL: +65 6338 3988 FAX: +65 6337 9989

LANDSCAPE CONSULTANT
DP GREEN PTE LTD
6 RAFFLES BOULEVARD
#02-249 MARINA SQUARE
SINGAPORE 039594
TEL: +65 6338 3988 FAX: +65 6337 9989

INTERIOR DESIGNER
DP DESIGN PTE LTD
6 RAFFLES BOULEVARD
#02-249 MARINA SQUARE
SINGAPORE 039594
TEL: +65 6338 3988 FAX: +65 6337 9989

QUANTITY SURVEYOR
AECOM COST CONSULTING AND PROJECT MANAGEMENT (S) PTE LTD
300 BEACH ROAD #03-00, THE CONCOURSE
SINGAPORE 199555
TEL: +65 62992466 FAX: +65 62990297

MECHANICAL & ELECTRICAL ENGINEER
MEIN-HARDT
Meinhardt (Singapore) Pte Ltd
168 Jalan Bukit Merah, #09-01, Surlana One
SINGAPORE 150168
TEL: +65 6273 5255 FAX: +65 6274 0788

CIVIL, STRUCTURAL & GEOTECHNICAL ENGINEER
MEIN-HARDT
Meinhardt (Singapore) Pte Ltd
168 Jalan Bukit Merah, #09-01, Surlana One
SINGAPORE 150168
TEL: +65 6273 5255 FAX: +65 6274 0788

PROJECT ARCHITECT
DP ARCHITECTS PTE LTD
6 RAFFLES BOULEVARD
#02-249 MARINA SQUARE
SINGAPORE 039594
TEL: +65 6338 3988 FAX: +65 6337 9989

DSTA
Defence Science & Technology Agency



PANG LU KIT
Programme Director (CMPB)
Project no.
D2011-00370-170

Project title
CONSTRUCTION OF 2 BLOCKS OF 13-STOREY OFFICE BUILDINGS WITH A BASEMENT AND 1 BLOCK OF 10-STOREY MULTI-STOREY CARPARK AT HILLVIEW LINK

Drawing title
**ELECTRICAL SERVICES
SINGLE LINE DIAGRAM (2 OF 28)**

	Initial	Date	Filename	D2011-00370-170/OT-E-107
Designed:	TKS	NOV 2024	Filename:	D2011-00370-170/OT-E-107
Drawn:	AAS	NOV 2024	Scale:	NTS

Drawing no.
D2011-00370-170/OT-E-107

Serial no.

THIS DRAWING IS THE PROPERTY OF DSTA. IF FOUND, PLEASE RETURN TO DSTA BUILDING AND INFRASTRUCTURE PROGRAMME CENTRE.
1 DEPOT ROAD, DEFENCE TECHNOLOGY TOWER A, SINGAPORE 109679.
REPRODUCTION OF DRAWING WITHOUT THE WRITTEN PERMISSION OF DSTA BI IS STRICTLY PROHIBITED. ANY UNAUTHORIZED REPRODUCTION OR POSSESSION SHALL BE DEALT WITH UNDER THE OFFICIAL SECRETS ACT.