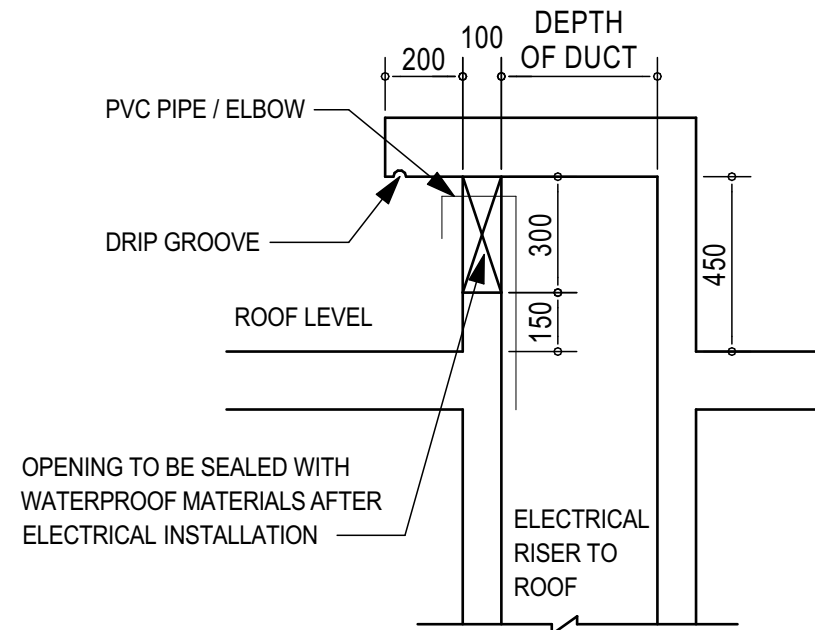
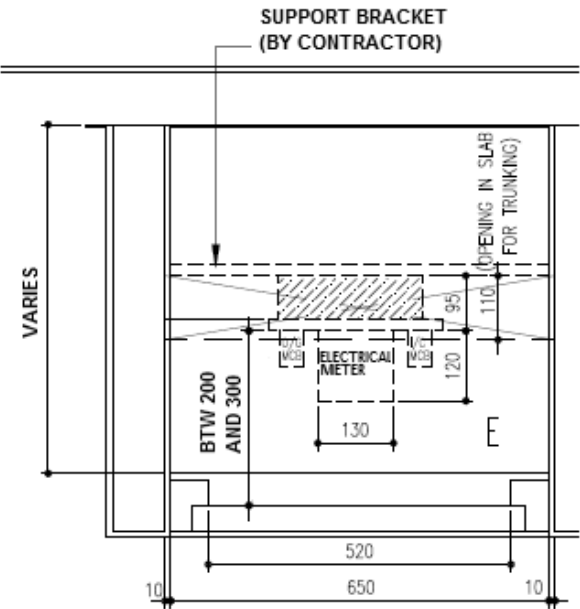


ELECTRICAL INSTALLATION					ELECTRICAL INSTALLATION				
DWG. NOS.	DRAWING TITLES	EST. BLK. NO.	CURRENT REVISION	DATE	DWG. NOS.	DRAWING TITLES	EST. BLK. NO.	CURRENT REVISION	DATE
001	CONTENTS OF CONTRACT DRAWINGS (PART 1 OF 2)				COMMERCIAL PLAZA BLOCK				
002	CONTENTS OF CONTRACT DRAWINGS (PART 2 OF 2)								
003	ELECTRICAL GENERAL NOTES & DETAILS				171	1ST STOREY FLOOR PLAN - CCC & PLAZA	148 & 149		
004	ELECTRICAL LEGEND				172	2ND STOREY FLOOR PLAN - CCC & PLAZA	148 & 149		
005	LAYOUT & KEY PLAN				173	3RD STOREY FLOOR PLAN - CCC & PLAZA	148 & 149		
006	UNDERGROUND PIPELINES AND MANHOLES FOR TELEPHONE SYSTEM				174	MAIN ROOF FLOOR PLAN - CCC	148		
007	ROUTING FOR GENERATOR SUPPLIES CABLES				175	PLAN OF LIFT MACHINE ROOM - CCC	148		
008	PIPING SYSTEM FOR UNDERGROUND H.T & L.T. RETICULATION CABLES				176	PLAN OF LIFT MACHINE ROOM ROOF - CCC	148		
009	FLOOR PLANS OF CABLE CHAMBER ROOM AND TRANSFORMER ROOM OF ELECTRICAL SUB-STATION 3	146			177	SINGLE LINE DIAGRAM OF MAIN SWITCHBOARD MSB'CCC&RNC'	148		
010	FLOOR PLANS OF SWITCH GEAR ROOM AND TRANSFORMER ROOM OF ELECTRICAL SUB-STATION 3	146			178	SINGLE LINE DIAGRAM OF ESSENTIAL SERVICE BOARD ESB'CCC&RNC'	148		
011	SECTIONS AND ELEVATIONS OF ELECTRICAL SUB-STATION 3	146			179	SINGLE LINE DIAGRAM OF DB'PL' & DB'EPL'	148		
012	ELECTRICAL INSTALLATION TO ELECTRICAL SUB-STATION 3	146			180	SINGLE LINE DIAGRAM OF CU'CC1, CU'CC2' & CU'CC3'	148		
013	FLOOR PLANS OF CABLE CHAMBER ROOM AND TRANSFORMER ROOM OF ELECTRICAL SUB-STATION 4	147			181	SCHEMATIC DIAGRAM OF OPTICAL FIBRE CABLING	148		
014	FLOOR PLANS OF SWITCH GEAR ROOM AND TRANSFORMER ROOM OF ELECTRICAL SUB-STATION 4	147			182	SINGLE LINE DIAGRAM OF MAIN SWITCHBOARD MSB'PLAZA'	149		
015	SECTIONS AND ELEVATIONS OF ELECTRICAL SUB-STATION 4	147			183	SINGLE LINE DIAGRAM OF DB'RG' FOR PLAZA & CCC	148		
016	ELECTRICAL INSTALLATION TO ELECTRICAL SUB-STATION 4	147			184	1ST STOREY FLOOR PLAN	148		
017	DETAILS OF DOORS FOR ELECTRICAL SUB-STATION (PART 1 OF 2), WOODEN MANDREL AND PVC COVER PLATES FOR HT CABLES				185	2ND STOREY FLOOR PLAN	148		
018	DETAILS OF DOORS FOR ELECTRICAL SUB-STATION (PART 2 OF 2)				186	3RD STOREY FLOOR PLAN	148		
019	DETAILS OF PC VENTS, GLASS BLOCK, ALUMINIUM LOUVRED, PIPE RAILINGS AND APPENDIX 15 FOR ELECTRICAL SUBSTATION				187	MAIN ROOF FLOOR PLAN	148		
020	DETAILS FOR ELECTRICAL SUB-STATION				188	PLAN OF LIFT MACHINE ROOM	148		
OUTDOOR FACILITIES					189	ELECTRICAL INSTALLATION TO RESIDENTS' NETWORK CENTRE	148		
021	SITE PLAN (AMENITIES)				190	AUTOMATIC FIRE ALARM SYSTEM TO RESIDENTS' NETWORK CENTRE	148		
022	SINGLE LINE DIAGRAM 1 - LANDSCAPE LIGHTINGS				191	SCHEMATIC DIAGRAM OF AUTOMATIC FIRE ALARM SYSTEM	148		
023	SINGLE LINE DIAGRAM 2 - LANDSCAPE LIGHTINGS				192	ELEVATION 1 & 2 (LIGHTNING PROTECTION SYSTEM)	148 & 149		
024	FLOOR, ROOF PLAN AND SECTIONS OF PRECINCT PAVILION 3	147			193	ELEVATION 3 & 4 (LIGHTNING PROTECTION SYSTEM)	148 & 149		
025	FLOOR, ROOF PLAN AND SECTIONS OF PRECINCT PAVILION 4	150			DWELLING UNIT				
026	DROP-OFF PORCH 4, HIGH LINKWAY & LINK WAY 10 FLOOR PLAN				201	TYPICAL FLOOR PLAN OF 2-ROOM FLAT TYPE 2R1 (2-PANEL SLIDING DOOR)	-		
027	DROP-OFF PORCH 4, HIGH LINKWAY & LINK WAY 10 ROOF PLAN				202	TYPICAL FLOOR PLAN OF 2-ROOM FLAT TYPE 2R1 (3-PANEL SLIDING DOOR)	-		
028	HIGH LINKWAY, LINK WAY 8 FLOOR AND ROOF PLAN				203	TYPICAL FLOOR PLAN OF 2-ROOM FLAT TYPE 2R2-1 (2-PANEL SLIDING DOOR)	-		
029	LINK WAY 12 FLOOR AND ROOF PLAN				204	TYPICAL FLOOR PLAN OF 2-ROOM FLAT TYPE 2R2-1 (3-PANEL SLIDING DOOR)	-		
030	HIGH LINKWAY, DROP-OFF PORCH 6 FLOOR AND ROOF PLAN				205	TYPICAL FLOOR PLAN OF 3-ROOM FLAT TYPE	-		
STANDARD DRAWINGS					206	TYPICAL FLOOR PLAN OF 4-ROOM FLAT TYPE	-		
051	TYPICAL LAMP POST (3/3.5/4m) FOOTING AND FOUNDATION FOR FOOTPATH / LANDSCAPE LIGHTING AT TURFING AREA AND CONCRETE PAVEMENT								
052	TYPICAL LAMP POST (6m) FOOTING AND FOUNDATION FOR DRIVEWAY / SERVICE ROAD AT TURFING AREA AND CONCRETE PAVEMENT								
053	TYPICAL LAMP POST (6m) FOOTING AND FOUNDATION FOR HARD COURT AT TURFING AREA AND CONCRETE PAVEMENT								
054	TYPICAL DETAIL OF INSTALLATION TO LIGHTNING PROTECTION SYSTEM CAPPING AND WELDING TO REBAR								
055	DETAILS OF PIPE SLEEVE PENETRATION FOR CABLES FOR MNO								
056	TYPICAL LIGHTNING PROTECTION SYSTEM FOR COVERED LINKWAY								
057	TYPICAL LIGHTING AND ELECTRICAL INSTALLATION DETAILS FOR COVERED LINKWAY/BUSTOP/TAXI/PUDO SHELTER								
058	TYPICAL DETAIL OF LTAOG BOX (COVERED LINKWAY AND BUS STOP)								
RESIDENTIAL									
101	1ST STOREY FLOOR PLAN	146A							
102	2ND STOREY FLOOR PLAN	146A							
103	3RD TO 18TH, 20TH TO 38TH, 40TH TO 48TH TYPICAL STOREY FLOOR PLAN	146A							
104	19TH STOREY FLOOR PLAN WITH SKY TERRACE	146A							
105	39TH STOREY FLOOR PLAN WITH SKY TERRACE	146A							
106	49TH STOREY FLOOR PLAN	146A							
107	MAIN ROOF PLAN	146A							
108	WATER TANK, BOOSTER & FHR HOSEREEL PUMP SPACES	146A							
109	LIFT MACHINE ROOM FLOOR PLAN AND ROOF PLAN OF BOOSTER PUMP SPACES AND STAIRCASE S2	146A							
110	ROOF PLAN OF LIFT MACHINE ROOM AND STAIRCASE S1	146A							
111	SINGLE LINE DIAGRAM OF MAIN SWITCHBOARD 1 (PART 1 OF 2)	146A							
112	SINGLE LINE DIAGRAM OF MAIN SWITCHBOARD 1 (PART 2 OF 2)	146A							
113	SINGLE LINE DIAGRAM OF MAIN SWITCHBOARD 2	146A							
114	SINGLE LINE DIAGRAM OF MAIN SWITCHBOARD 3	146A							
115	SINGLE LINE DIAGRAM OF DISTRIBUTION BOARD (DB 'PL')	146A							
116	SINGLE LINE DIAGRAM OF EMERGENCY DISTRIBUTION BOARD (DB 'EPL')	146A							
117	SCHEMATIC DIAGRAM OF OPTICAL FIBRE CABLING (PART 1 OF 2)	146A							
118	SCHEMATIC DIAGRAM OF OPTICAL FIBRE CABLING (PART 2 OF 2)	146A							
119	1ST STOREY FLOOR PLAN	147A							
120	2ND STOREY FLOOR PLAN	147A							
121	3RD TO 18TH, 20TH TO 38TH, 40TH TO 48TH TYPICAL STOREY FLOOR PLAN	147A							
122	19TH STOREY FLOOR PLAN WITH SKY TERRACE	147A							
123	39TH STOREY FLOOR PLAN WITH SKY TERRACE	147A							
124	49TH STOREY FLOOR PLAN	147A							
125	MAIN ROOF PLAN	147A							
126	WATER TANK, BOOSTER & FHR HOSEREEL PUMP SPACES	147A							
127	LIFT MACHINE ROOM FLOOR PLAN AND ROOF PLAN OF BOOSTER PUMP SPACES AND STAIRCASE S2	147A							
128	ROOF PLAN OF LIFT MACHINE ROOM AND STAIRCASE S1	147A							
129	SINGLE LINE DIAGRAM OF MAIN SWITCHBOARD 1 (PART 1 OF 2)	147A							
130	SINGLE LINE DIAGRAM OF MAIN SWITCHBOARD 1 (PART 2 OF 2)	147A							
131	SINGLE LINE DIAGRAM OF MAIN SWITCHBOARD 2	147A							
132	SINGLE LINE DIAGRAM OF MAIN SWITCHBOARD 3	147A							
133	SINGLE LINE DIAGRAM OF DISTRIBUTION BOARD (DB 'PL')	147A							
134	SINGLE LINE DIAGRAM OF EMERGENCY DISTRIBUTION BOARD (DB 'EPL')	147A							
135	SCHEMATIC DIAGRAM OF OPTICAL FIBRE CABLING (PART 1 OF 2)	147A							
136	SCHEMATIC DIAGRAM OF OPTICAL FIBRE CABLING (PART 2 OF 2)	147A							
137	1ST STOREY FLOOR PLAN	148A							
138	2ND STOREY FLOOR PLAN	148A							
139	3RD TO 18TH, 20TH TO 38TH, 40TH TO 48TH TYPICAL STOREY FLOOR PLAN	148A							
140	19TH STOREY FLOOR PLAN (SKY TERRACE)	148A							
141	39TH STOREY FLOOR PLAN (SKY TERRACE)	148A							
142	49TH STOREY FLOOR PLAN (TOPMOST FLOOR)	148A							
143	MAIN ROOF PLAN	148A							
144	WATER TANK, BOOSTER & FHR HOSEREEL PUMP SPACES	148A							
145	LIFT MACHINE ROOM FLOOR PLAN AND STAIRCASE	148A							
146	ROOF PLAN OF LIFT MACHINE ROOM AND STAIRCASE	148A							
147	SINGLE LINE DIAGRAM OF MAIN SWITCHBOARD 1 (PART 1 OF 2)	148A							
148	SINGLE LINE DIAGRAM OF MAIN SWITCHBOARD 1 (PART 2 OF 2)	148A							
149	SINGLE LINE DIAGRAM OF MAIN SWITCHBOARD 2	148A							
150	SINGLE LINE DIAGRAM OF MAIN SWITCHBOARD 3	148A							
151	SINGLE LINE DIAGRAM OF DISTRIBUTION BOARD (DB 'PL')	148A							
152	SINGLE LINE DIAGRAM OF EMERGENCY DISTRIBUTION BOARD (DB 'EPL')(PART 1 OF 2)	148A							
153	SINGLE LINE DIAGRAM OF EMERGENCY DISTRIBUTION BOARD (DB 'EPL')(PART 2 OF 2)	148A							
154	SCHEMATIC DIAGRAM OF OPTICAL FIBRE CABLING	148A							
155	TYPICAL SINGLE LINE DIAGRAM TO SERVICES ROOM	148A							
156	TYPICAL SINGLE LINE DIAGRAM TO SERVICES ROOM	148A							
157	TYPICAL SINGLE LINE DIAGRAM TO SERVICES ROOM	148A							
158	ELECTRICAL INSTALLATION TO MDF ROOM	146							
159	ELECTRICAL INSTALLATION TO TER	146A							
160	ELECTRICAL INSTALLATION TO TER	148A							
161	DETAILS OF MDF, TER & TELECOM RISER								

ELECTRICAL GENERAL NOTES

[illegible]

TYPICAL DETAIL OF DOG HOUSE OF ELECTRICAL
CABLES ON ROOF
SCALE: N.T.S.



TYPICAL DETAIL OF ELECTRICAL RISER /
METER DUCT
SCALE: N.T.S.

TENDER DRAWING



HDB Hub 480 Lorong 6 Toa Payoh
Singapore 310480

OWNER SIGNATURE:

PRECINCT NAME:	BTO
----------------	-----

PROJECT TITLE
PROPOSED PUBLIC HOUSING DEVELOPMENT COMPRISING 2 BLKS OF 40-STY, 1 BLK OF 49-STY RESIDENTIAL BUILDING (TOTAL 1021 UNITS), 1 BLK OF 7-STY MSCP WITH ROOF GARDEN, SOCIAL COMMUNITY FACILITIES, 2 ESS & 2 PRECINCT PAVILIONS AT REDHILL CLOSE

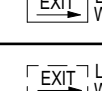
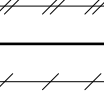
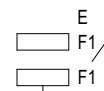
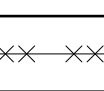
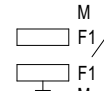
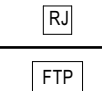
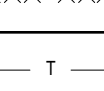
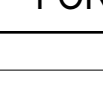
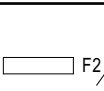
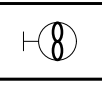
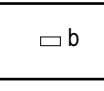
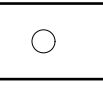
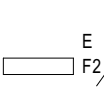
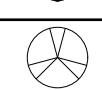
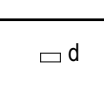
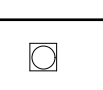
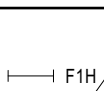
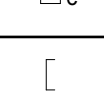
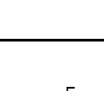
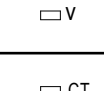
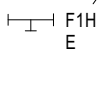
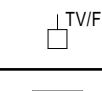
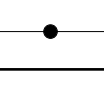
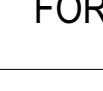
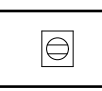
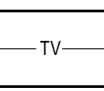
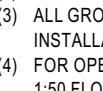
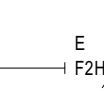
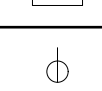
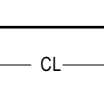
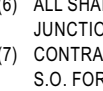
 
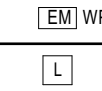
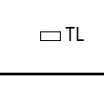
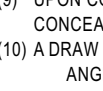
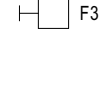
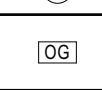
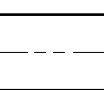
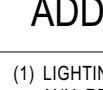
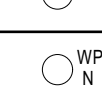
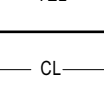
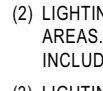
 
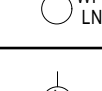
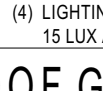
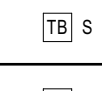
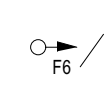
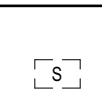
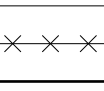
 
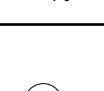
LOT NO.: 04265M, 04262X, 03775A, 04261N, 04260K, 04259X, 04257K, 04255T, 04254P, 04253V, 04256A, 04258N, 04252W, 02983K, 04245X, 04249W, 04246L,	MUKIM NO.: 01
---	------------------

BUKIT MERAH C73 PART 2

DRAWING TITLE _____

ELECTRICAL GENERAL NOTES & DETAILS

REV	AMENDMENT	DATE	DRAWN BY	CHECKED BY	DE	QP	REV	AMENDMENT	DATE	DRAWN BY	CHECKED BY	DE	QP	DRAWING NO.: HB-D24026-ME-003	REVISION:
														SCALE: N.T.S.	DATE: JUN 2025
														DRAWN BY: AYE MIN LWIN	CHECKED BY: NG CHER HEONG
														NG CHER HEONG DESIGN ENGINEER	NG CHER HEONG QUALIFIED PERSON
REFERENCE														THE OWNERSHIP OF THE COPYRIGHT IN THIS DRAWING IS RETAINED BY HOUSING & DEVELOPMENT BOARD WHOSE CONSENT MUST BE SOUGHT BEFORE ANY USE OR REPRODUCTION OF THE DRAWING OR ANY PART THEREOF CAN BE MADE.	

ELECTRICAL LEGEND (Applicable for residential blocks / outdoor lighting installation / multi storey carpark)										FOR RESIDENTIAL/COMMERCIAL BLOCKS									
SPECIFIC ELECTRICAL LEGEND					GENERAL ELECTRICAL LEGEND					LEGEND OF ELECTRICAL TRUNKING/CONDUIT ROUTE					LEGEND OF CONCEAL DETAILS FOR ELECTRICAL WIRINGS				
	CORRIDOR/STAIRCASE/COMMERCIAL HDB APPROVED 2 FEET SURFACE/SUSPENDED MOUNTED SLIM PROFILE LED LIGHT FITTING RATED LESS THAN 12W (>700LM & <900LM) C/W SMART LIGHTING SYSTEM, SHEET STEEL HOUSING, LED MODULE, DIFFUSER, IP54 OR OTHER APPROVED		CARPARK CAR WASH BAY HDB APPROVED 4 FEET SURFACE/SUSPENDED MOUNTED SLIM PROFILE LED LIGHT FITTING RATED LESS THAN 24W (>200LM & <300LM) C/W SMART LIGHTING SYSTEM, SHEET STEEL HOUSING, LED MODULE, DIFFUSER, IP55 OR OTHER APPROVED		UNDERGROUND UPVC PIPE FOR UNDERGROUND CABLE RUNNING BELOW COURTYON/ CONC. PAVEMENT/LINKWAY UNLESS OTHERWISE STATED. ONE NO. OF 90mm DIA UPVC SPAKE PIPE IS TO BE PROVIDED		WALL/CEILING MOUNTED WHITE LED MAINTAINED WEATHERPROOF EMERGENCY EXIT LIGHT (SINGLE SIDED, WITHOUT DIRECTIONAL ARROWS) C/W 2 HOURS NI-CD BATTERIES, IP65 OR OTHER APPROVED		DOUBLE LAYER METAL TRUNKING ROUTE FOR ELECTRICAL MAINS		FIRE RATED BOX-UP								
	CORRIDOR/STAIRCASE HDB APPROVED 2 FEET SURFACE/SUSPENDED MOUNTED SLIM PROFILE LED LIGHT FITTING RATED LESS THAN 12W (>700LM & <900LM) C/W SMART LIGHTING SYSTEM, SHEET STEEL HOUSING, LED MODULE, DIFFUSER, IP54, EMERGENCY BATTERY FOR 2 HRS OPERATION OR OTHER APPROVED		CARPARK CAR WASH BAY HDB APPROVED 4 FEET SURFACE/SUSPENDED MOUNTED SLIM PROFILE LED LIGHT FITTING RATED LESS THAN 24W (>200LM & <300LM) C/W SMART LIGHTING SYSTEM, SHEET STEEL HOUSING, LED MODULE, DIFFUSER, IP55, EMERGENCY BATTERY FOR 2 HRS OPERATION OR OTHER APPROVED		INCOMING SERVICE CABLE		TELEPHONE BLOCK TERMINAL		SINGLE LAYER METAL TRUNKING ROUTE FOR ELECTRICAL MAINS										
	STAIRCASE/HALF LANDING / REFUSE CHUTE HDB APPROVED 2 FEET SURFACE/SUSPENDED MOUNTED SLIM PROFILE LED LIGHT FITTING RATED LESS THAN 12W (>700LM & <900LM) C/W SMART LIGHTING SYSTEM, SHEET STEEL HOUSING, LED MODULE, DIFFUSER, IP54 OR OTHER APPROVED		SURFACE MOUNTED 2FT LED T8 LIGHT FITTING <=12W, >=1100mm, C/W HIGH QUALITY SHEET STEEL HOUSING AND EPOXY POWDER COATED IN WHITE, IP54. TO BE SELECTED FROM HDB'S MATERIAL LIST OR OTHER APPROVED & SHALL BE BATCH TESTED.		WEATHERPROOF CABLE TERMINATION BOX C/W 6A HRC FUSE AND HEXAGON HEAD SCREWS FOR COVER		RJ45 OUTLET		025mm METAL CONDUIT FOR TELEPHONE POINT AT LIFT MACHINE ROOM		CIRCULAR JUNCTION BOX								
	1ST STOREY/SCF HDB APPROVED 4 FEET SURFACE/SUSPENDED MOUNTED SLIM PROFILE LED LIGHT FITTING RATED LESS THAN 24W (>1400LM & <1600LM) C/W SMART LIGHTING SYSTEM, SHEET STEEL HOUSING, LED MODULE, DIFFUSER, IP54 OR OTHER APPROVED		SURFACE MOUNTED 2FT LED T8 LIGHT FITTING <=12W, >=1100mm, C/W HIGH QUALITY SHEET STEEL HOUSING AND EPOXY POWDER COATED IN WHITE, IP54. TO BE SELECTED FROM HDB'S MATERIAL LIST OR OTHER APPROVED & SHALL BE BATCH TESTED.		WEATHERPROOF 13AMP SWITCH SOCKET OUTLET C/W SCREW CAP		0400mm WALL BRACKET FAN SIMILAR TO 'XOX' C/W PULL CORD SWITCH OR OTHER APPROVED		METAL TRUNKING THRU' CEILING/FLOOR SLAB FOR ELECTRICAL MAINS (325(W) x 80(D) OPENING THRU' CEILING SLAB)		VERTICAL CONCEALED CONDUIT								
	1ST STOREY/SCF HDB APPROVED 4 FEET SURFACE/SUSPENDED MOUNTED SLIM PROFILE LED LIGHT FITTING RATED LESS THAN 24W (>1400LM & <1600LM) C/W SMART LIGHTING SYSTEM, SHEET STEEL HOUSING, LED MODULE, DIFFUSER, IP54, EMERGENCY BATTERY FOR 2 HRS OPERATION OR OTHER APPROVED		SURFACE MOUNTED 2FT LED T8 LIGHT FITTING <=12W, >=1100mm, C/W HIGH QUALITY SHEET STEEL HOUSING AND EPOXY POWDER COATED IN WHITE, IP54. TO BE SELECTED FROM HDB'S MATERIAL LIST OR OTHER APPROVED & SHALL BE BATCH TESTED.		WEATHERPROOF 15AMP SWITCH SOCKET OUTLET C/W SCREW CAP		018mm WALL/COLUMN MOUNTED OSCILLATING INDUSTRIAL FAN WITH FULL FINGER GUARD SHROUD AND OVERHEAT PROTECTION		METAL TRUNKING THRU' CEILING/FLOOR SLAB FOR ELECTRICAL MAINS (80(W) x 60(D) OPENING THRU' CEILING SLAB)		CIRCULAR JUNCTION BOX C/W VERTICAL CONDUIT AT 2.5m FROM FINISHED FLOOR LEVEL								
	CARPARK/SERVICES ROOM HDB APPROVED 2 FEET SURFACE/SUSPENDED MOUNTED SLIM PROFILE LED LIGHT FITTING RATED LESS THAN 12W (>1100LM & <1500LM) C/W SMART LIGHTING SYSTEM, SHEET STEEL HOUSING, LED MODULE, DIFFUSER, IP54 OR OTHER APPROVED		SURFACE MOUNTED 2x 4FT LED T8 LIGHT FITTING <=20W, >=2200mm, C/W HIGH QUALITY SHEET STEEL HOUSING AND EPOXY POWDER COATED IN WHITE, IP54. TO BE SELECTED FROM HDB'S MATERIAL LIST OR OTHER APPROVED & SHALL BE BATCH TESTED.		13AMP METAL CLAD SWITCH SOCKET OUTLET TO BE MOUNTED AT HIGH LEVEL		BLOCK TERMINAL IN METAL ENCLOSURE C/W BUILT-IN LOCK & KEY		025mm OPENING THRU' R.C. BEAM/WALL		NON-SHRINK GROUT TEMPLATE (GRADE 30) C/W BOLTS & NUTS ON TOP OF RC STUMP (FOR PLANTER AREA)								
	CARPARK/SERVICES ROOM HDB APPROVED 2 FEET SURFACE/SUSPENDED MOUNTED SLIM PROFILE LED LIGHT FITTING RATED LESS THAN 12W (>1100LM & <1500LM) C/W SMART LIGHTING SYSTEM, SHEET STEEL HOUSING, LED MODULE, DIFFUSER, IP54, EMERGENCY BATTERY FOR 2 HRS OPERATION OR OTHER APPROVED		SURFACE MOUNTED 2x 4FT LED T8 LIGHT FITTING <=20W, >=2200mm, C/W HIGH QUALITY SHEET STEEL HOUSING AND EPOXY POWDER COATED IN WHITE, IP54. TO BE SELECTED FROM HDB'S MATERIAL LIST OR OTHER APPROVED & SHALL BE BATCH TESTED.		13AMP SWITCH SOCKET OUTLET IN RECESSED WEATHERPROOF METAL ENCLOSURE (IP65)		TELEVISION OUTLET		75x 75 METAL TRUNKING FOR SCV/MATV		TELEPHONE CABLE TRAY								
	CARPARK/SERVICES ROOM HDB APPROVED 4 FEET SURFACE/SUSPENDED MOUNTED SLIM PROFILE LED LIGHT FITTING RATED LESS THAN 24W (>2200LM & <3000LM) C/W SMART LIGHTING SYSTEM, SHEET STEEL HOUSING, LED MODULE, DIFFUSER, IP54 OR OTHER APPROVED		SURFACE MOUNTED 4FT LED T8 LIGHT FITTING <=20W, >=2200mm, C/W HIGH QUALITY SHEET STEEL HOUSING AND EPOXY POWDER COATED IN WHITE, IP54. TO BE SELECTED FROM HDB'S MATERIAL LIST OR OTHER APPROVED & SHALL BE BATCH TESTED.		15AMP METAL CLAD SWITCH SOCKET OUTLET IN RECESSED WEATHERPROOF METAL ENCLOSURE (IP65)		CORRIDOR LAMP C/W BUILT-IN BUZZER SIMILAR TO ISPL-CLV02		150mm CABLE TRAY FOR TV		METAL TRUNKING THRU' CEILING/FLOOR SLAB FOR TELEPHONE MAINS (200(W) x 80(H) OPENING THRU' ALL R.C BEAMS/WALLS)								
	CARPARK/SERVICES ROOM HDB APPROVED 4 FEET SURFACE/SUSPENDED MOUNTED SLIM PROFILE LED LIGHT FITTING RATED LESS THAN 24W (>2000LM & <3000LM) C/W SMART LIGHTING SYSTEM, SHEET STEEL HOUSING, LED MODULE, DIFFUSER, IP54, EMERGENCY BATTERY FOR 2 HRS OPERATION OR OTHER APPROVED		SURFACE MOUNTED 4FT LED T8 LIGHT FITTING <=20W, >=2200mm, C/W HIGH QUALITY SHEET STEEL HOUSING AND EPOXY POWDER COATED IN WHITE, IP54. TO BE SELECTED FROM HDB'S MATERIAL LIST OR OTHER APPROVED & SHALL BE BATCH TESTED.		16A INDUSTRIAL SOCKET		RECESSED WEATHERPROOF CABLE TERMINATION BOX C/W 6A HRC FUSE AND HEXAGON HEAD SCREWS FOR COVER		WEATHERPROOF ELECTRICAL METER BOX		DIGITAL PHOTOCCELL LIGHT SENSOR								
	HIGH VOID / HIGH LINKWAY CAT E2 SURFACE MOUNTED LED LUMINAIRE RATED NOT MORE THAN 30W (>2400lm), DIE-CAST ALUMINIUM ALLOY, RESISTANT TO SUPERIOR CORROSION PROTECTION, IP65, C/W SMART LIGHTING SYSTEM, MOUNTED AT 3M HEIGHT, COLOUR TO ARCHITECT'S SELECTION OR OTHER APPROVED		SURFACE MOUNTED 4FT LED T8 LIGHT FITTING <=20W, >=2200mm, C/W HIGH QUALITY SHEET STEEL HOUSING AND EPOXY POWDER COATED IN WHITE, IP65. TO BE SELECTED FROM HDB'S MATERIAL LIST OR OTHER APPROVED & SHALL BE BATCH TESTED.		TWO WAY SWITCH		ELECTROMAGNETIC LOCK		WEATHERPROOF 0.6 BOX (IP65 TO BS 5420 & EPOXY POWDER COATED MOUNTED ON CONCRETE PEDESTAL TO ENGR'S APPROVAL, ACTUAL LOCATION TO BE DETERMINED AT SITE)		WEATHERPROOF LIGHTING POINT FOR ILLUMINATED BLOCK SIGNAGE C/W POLARISE PLUS, SOCKET WITH CONCEALED CONDUIT TO CEILING & TO BE INTEGRATED WITH SMART LIGHTING SYSTEM								
	REFLECTED CEILING (LIFT LOBBY) HDB APPROVED LED DOWN LIGHT WITH RATED LESS THAN 12W (>600LM) COLOUR RENDERING INDEX ABOVE 75, CORRELATED COLOUR TEMPERATURE OF 3500K, C/W SMART LIGHTING REQUIREMENTS AND PASS BATCH TESTING, COMPLETE WITH SUSPENSION CABLE AND SUPPORTING SYSTEM TO CEILING SOFIT OR OTHER APPROVED		SURFACE MOUNTED 4FT LED T8 LIGHT FITTING <=20W, >=2200mm, C/W HIGH QUALITY SHEET STEEL HOUSING AND EPOXY POWDER COATED IN WHITE, IP65. TO BE SELECTED FROM HDB'S MATERIAL LIST OR OTHER APPROVED & SHALL BE BATCH TESTED.		ONE WAY SINGLE POLE SWITCH		WEATHERPROOF LIGHTING POINT FOR ILLUMINATED BLOCK SIGNAGE C/W POLARISE PLUS, SOCKET WITH CONCEALED CONDUIT TO CEILING & TO BE INTEGRATED WITH SMART LIGHTING SYSTEM		
	TRELLIS/SHELTER/ROOF GARDEN CAT E1 SURFACE MOUNTED LED LUMINAIRE NOT MORE THAN 10W (>=800lm), DIE-CAST ALUMINIUM BODY AND RM, RESISTANT TO SUPERIOR CORROSION PROTECTION, DIMMABLE DRIVER, C/W SMART LIGHTING SYSTEM, IP65 OR OTHER APPROVED, COLOUR TO ARCHITECT'S SPECIFICATION		CENTRAL SPINE AT 1ST STOREY / FAMILY CABANA / DROP-OFF PORCH SURFACE MOUNTED UP - DOWN LED LUMINAIRE RATED 37.2W, C/W DIMMABLE DRIVER, SMART LIGHTING SYSTEM AND IP65, COLOR TEMPERATURE OF 3000K, TO READ IN CONJUNCTION WITH ARCHITECT'S SPECIFICATION OR EQUIVALENT		WEATHERPROOF REMOTE ON/OFF TOGGLE-SWITCH C/W LED/NEON INDICATOR		LIGHTING POINT CONSISTING OF PLUG & SOCKET TERMINAL HOUSED IN GALVANISED STEEL BOX		TERMINAL BLOCK FOR FUTURE CONNECTION IN LOCKABLE ENCLOSURE (IP 55) MOUNTED AT 2.2m (FOR SMART LIGHTING SYSTEM)		TERMINAL BLOCK FOR FUTURE CONNECTION IN LOCKABLE ENCLOSURE (IP 65) MOUNTED AT 2.2m (FOR SMART WATER PRIVATE METER)								
	DRIVE WAY/SERVICE ROAD CAT ALED LUMINAIRE NOT MORE THAN 30W LED LAMP (>=2500lm), DIE-CAST ALUMINIUM ALLOY FRAME AND COVER, C/W SMART LIGHTING SYSTEM, MOUNTED ON 8M POLE OR SURFACE MOUNTED, WITH BRACKET ARM OF UP TO 0.6m, IP66 OR OTHER APPROVED, COLOUR TO ARCHITECT'S SPECIFICATION		CENTRAL SPINE AT 2ND STOREY BOLLARD LED LUMINAIRE RATED 15W, C/W DIMMABLE DRIVER, SMART LIGHTING SYSTEM AND IP66, COLOR TEMPERATURE OF 3000K, TO READ IN CONJUNCTION WITH ARCHITECT'S SPECIFICATION OR EQUIVALENT		WEATHERPROOF REMOTE ON/OFF TOGGLE-SWITCH C/W LED/NEON INDICATOR		METAL CLAD ISOLATOR SWITCH		SPACE FOR SMART CONTROLLER SPACE PROVISION OF AT LEAST 300mm(L) x 250mm(W) & 200mm(D) FOR THE SURFACE MOUNTED SMART CONTROLLER OR GATEWAY TO BE MOUNTED AT A MINIMUM HEIGHT OF 2200mm (EXACT LOCATION IS SUBJECT TO CONFIRMATION BY ARCHT)		SPACE FOR ADAPTOR MODULE SPACE PROVISION OF AT LEAST 300mm(L) x 220mm(W) & 200mm(D) FOR THE SURFACE MOUNTED ADAPTOR MODULE OR GATEWAY TO BE MOUNTED AT A MINIMUM HEIGHT OF 2200mm (EXACT LOCATION IS SUBJECT TO CONFIRMATION BY ARCHT)								
	LANDSCAPE/FOOTPATH/MSCP ROOF GARDEN CAT CLED LUMINAIRE NOT MORE THAN 20W (>=1000lm), DIE-CAST ALUMINIUM ALLOY, SUPERIOR CORROSION PROTECTION, DIMMABLE DRIVER, C/W SMART LIGHTING SYSTEM, LED CONCEPT OPTICS FOR SUPERIOR ILLUMINATION AND GLARE CONTROL, MOUNTED ON 3.5M POLE OR SURFACE MOUNTED ON 4.5M WITH BRACKET ARM OF UP TO 1.0m, IP68 OR OTHER APPROVED, COLOUR TO ARCHITECT'S SPECIFICATION		IT/LINKWAY 1TA APPROVED 2 FEET SURFACE MOUNTED SLIM PROFILE LED LIGHT FITTING RATED 7W, C/W SHEET STEEL HOUSING, LED MODULE, DIFFUSER, IP54		WEATHERPROOF ISOLATOR SWITCH		20A DP ISOLATOR WITH MASTER KEY SWITCH (FOR CABLE TV)		TWO-WAY FIREMEN INTERCOM HANDSET (EXACT LOCATION TO BE DETERMINED ON SITE)		CEILING MOUNTED MOTION SENSOR								
	PLAYGROUND/FITNESS STATION CAT CLED LUMINAIRE NOT MORE THAN 36W (>=3500lm), DIE-CAST ALUMINIUM ALLOY, SUPERIOR CORROSION PROTECTION, DIMMABLE DRIVER, C/W SMART LIGHTING SYSTEM, LED CONCEPT OPTICS FOR SUPERIOR ILLUMINATION AND GLARE CONTROL, SURFACE MOUNTED OR MOUNTED ON 3.5M POLE, IP68 OR OTHER APPROVED, COLOUR TO ARCHITECT'S SPECIFICATION		DROP-OFF PORCH CEILING MOUNTED LED LUMINAIRE RATED 10.5W, C/W DIMMABLE DRIVER, SMART LIGHTING SYSTEM AND IP65, COLOR TEMPERATURE OF 3000K, TO READ IN CONJUNCTION WITH ARCHITECT'S SPECIFICATION OR EQUIVALENT		WEATHERPROOF 20A DP ISOLATOR WITH MASTER KEY SWITCH (FOR CABLE CATV)		CONSUMER UNIT		SMART MAIN SWITCHBOARD		SMART ESSENTIAL SERVICE BOARD								
	PRECINCT MARKER SURFACE LED MOUNTED LUMINAIRE NOT MORE THAN 22W (>=2000lm), DIE-CAST ALUMINIUM ALLOY, SUPERIOR CORROSION PROTECTION, MOUNTING BRACKET, IK07, DIMMABLE DRIVER, IP66 OR OTHER APPROVED, COLOUR TO ARCHITECT'S SPECIFICATION		ROOF 220-70VAC MEDIUM INTENSITY RED LED AVIATION OBSTRUCTION LIGHT (AOL) AND 12V DC LOW INTENSITY RED LED AOL MOUNTED ON A HOT-DIP GALVANISED DOUBLE ARM STEEL BRACKET FIXED RIGIDLY ON A LIGHTSTAFF. THE 7 AOL'S SHALL BE CONNECTED TO A CONTROL CIRCUIT C/W AUTO CHANGE OVER RELAY FOR FAULTY LAMP, STANDBY BATTERY & CHARGER FOR EMERGENCY BACK UP OF 12V DC LED AOL, LIGHT SENSITIVE SWITCHING LSS IC200 WITH PHOTOCELL, FAULT/KEEP RELAY AND REMOTE MONITORING PANEL INCLUDING ALL CONNECTIONS AND ACCESSORIES TO BE APPROVED, (ACTUAL LOCATION TO BE DETERMINED ON SITE)		DISTRIBUTION BOARD		METAL CLAD DISTRIBUTION BOARD		AVIATION OBSTRUCTION LIGHT CONTROL CIRCUIT PANEL		AVIATION OBSTRUCTION LIGHT REMOTE MONITORING PANEL								
	PRECINCT PAVILION 4 FEET SURFACE/SUSPENDED MOUNTED SLIM PROFILE LED LIGHT FITTING RATED LESS THAN 36W (>2200LM & <3800LM) C/W SMART LIGHTING SYSTEM, SHEET STEEL HOUSING, LED MODULE, DIFFUSER, IP54 OR OTHER APPROVED.		DROP-OFF PORCH / PRECINCT PAVILION SURFACE MOUNTED UP - DOWN LED LUMINAIRE RATED 18.6W, C/W DIMMABLE DRIVER, SMART LIGHTING SYSTEM AND IP65, COLOR TEMPERATURE OF 3000K, TO READ IN CONJUNCTION WITH ARCHITECT'S SPECIFICATION OR EQUIVALENT		WEATHERPROOF METAL CLAD CONSUMER UNIT														

